

APPENDIX D

ROCK SAMPLE DATA SHEET

[illegible]

APPENDIX E

XRD RESULTS

WESTERN MINING CORPORATION LIMITED

EXPLORATION DIVISION

X.R.D. REPORTAREA: ANDAMOOKA E.L. 190 - 4101 SUBMITTED BY: D.F. EVANS DATE: 15/9/75

COMMENTS:

SAMPLE NO.	Musc	Qz	Dol	Mont	Mic	Kaol	Hem	Ab	Bar	Cal	I						
DA 16546	1	1	98	-	-	-	-	-	-	-		RDD 1	6.20				
DA 16551	-	54	46	-	-	-	-	-	-	-		"	19.80				
DA 16556	-	-	99	1	-	-	-	-	-	-		"	29.57				
DA 16559	-	1	99	-	-	-	-	-	-	-		"	34.84				
DA 16600	-	97	<1	-	3	-	-	-	-	-		"	128.90				
DA 17110	-	88	-	-	-	8	4	-	-	-		"	201.96				
DA 17121	12	40	-	2	-	28	12	7	-	-		"	224.41				
DA 17153	9	51	-	3	-	17	14	6	-	-		"	290.62				
DA 17178	1	14	-	-	-	7	75	-	4	-		"	337.24				
DA 17184	19	72	-	-	-	-	8	-	-	-		"	348.50				
DA 17187	4	16	-	-	-	-	61	-	20	-		"	353.18				
DA 17194	10	52	-	-	-	-	32	-	-	6		"	367.23				
DA 17196	16	37	3	-	-	-	34	-	3	8		"	372.95				
DA 17203	10	44	-	-	-	-	40	-	6	-		"	386.98				
DA 17205	9	39	-	-	-	-	48	-	-	4		"	390.22				
DA 17215	8	44	8	-	10	-	13	10	8	-		"	409.60				
DA 17352	1	55	15	1	7	-	-	20	-	-		RDD 2	433.70				
DA 17354	-	3	96	-	-	-	-	1	-	-		"	439.00				
DA 17357	3	86	-	-	-	-	11	-	-	-		"	445.40				
DA 17376	5	75	-	-	-	-	20	-	-	-		"	482.30				

APPENDIX F

BULK DENSITY MEASUREMENTS



amdel

The Australian Mineral Development Laboratories

Flemington Street, Frewville, South Australia 5063
Phone Adelaide 79 1662, telex AA82520

Please address all correspondence to Frewville.
In reply quote: MT 3/10/1/0

14 October 1975

Dr D. Evans
Western Mining Corporation
Daveys Road
FLAGSTAFF HILL SA 5159

REPORT MT 1068/76

YOUR REFERENCE: Telephone call on 3/10/76.
SUBJECT: Density Determination.
MATERIAL: Six samples of Drill Core.
DATE RECEIVED: 3/10/75.
INFORMATION REQUIRED: Bulk density.

Investigation and Report by: Dr W.G. Spencer.

Officer in Charge, Materials Technology Section: Dr Graham L.F. Powell.

for F. R. Hartley
Director



1. INTRODUCTION

Six samples of drill-core were submitted on 3 October 1975 by Dr D. Evans, Western Mining Corporation, for urgent determinations of bulk density. This report confirms results telephoned through to Dr D. Evans on 3 October 1975.

2. PROCEDURES

The samples were weighed and soaked in water for two hours. They were weighed in the saturated, surface dry condition and suspended in water. The upthrust was determined. The samples were then dried and reweighed. The bulk density was calculated using the dry weight of core and the experimentally determined upthrust (bulk volume). The amount of water absorbed in the two hour soaking period (with reference to the dried core weights) is expressed as a two-hour cold water absorption.

3. RESULTS

The results are as follows :


<u>Sample RDD1</u>	<u>Bulk Density*</u>	<u>2-Hour cold water Absorption**</u> %
19.80	2.63	1.30
130.45	2.58	0.76
290.73	2.70	0.67
350.	3.05	1.00
410.3	2.81	0.37
472.70	2.60	0.80

* defined as $\frac{\text{dry weight}}{\text{'upthrust'}}$



when 'upthrust' is weight of displaced water.

** defined as $\frac{\text{saturated surface dry weight} - \text{dry weight}}{\text{dry weight}} \%$


dk.

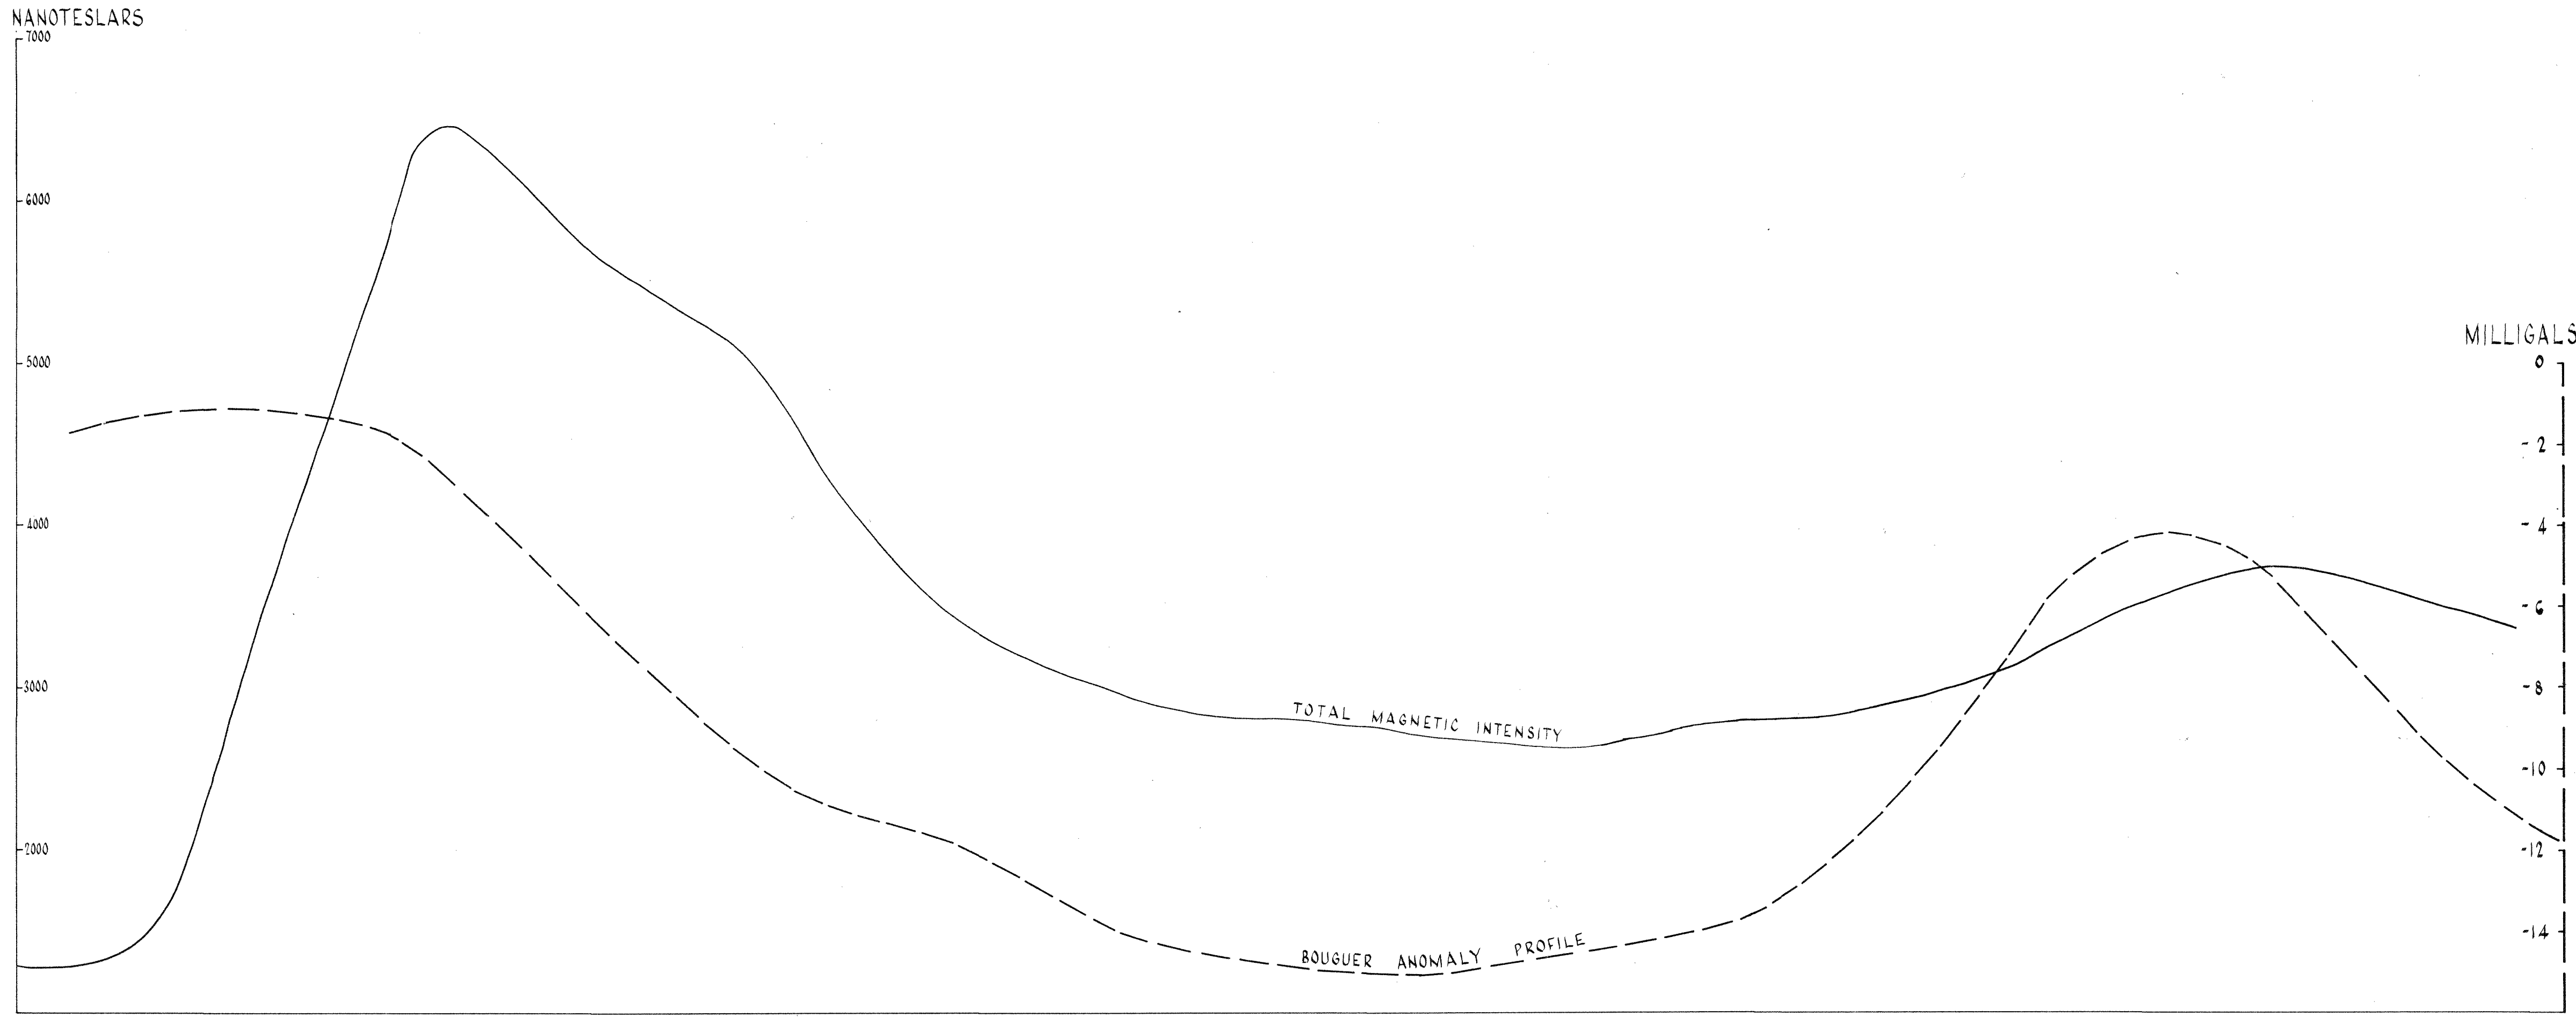

STRATIGRAPHIC COLUMN		
MARINONIAN TENT HILL FORMATION	CAMBRIAN	
	Eh Andamooka Limestone	- Grey, f.f.g. massively bedded dolomite plus dolomitic sandstone with cavities plus sandy clastic dolomite. Basal dolomite breccia.
	UPPER PROTEROZOIC	
	Ews Simmens (Arcoona) Quartzite	- White to grey m.g. well rounded sandstone and quartzite with choc. brown clay clots. Lesser red and purple and green siltstone interbeds. Minor low-angle cross-strat. Py in fractures and clots.
	Ewc Corraberra Sandstone	- Brown and red, m.g. well bedded to massive micaceous sandstone composed of quartz - fels? - hem - glauc?
	Ewt Tregolana (Woomera) Shale	- Interbedded choc. brown and green shales and siltstones with lesser v.f.g. to f.g. cross-strat. sandstone. Shales normally laminated, but up to 2 cm.
	E Quartzite	- Grey f.m.g. hem. arkosic quartzite; massive bedding, non-mag. Graded type bedding present with f.m.g. massive grey quartzite grading upwards into dark brown micaceous siltstone.
	E Dolomite	- White to pink, well bedded clastic dolomite with abundant gyp. both as beds and open space filling. Non-mag.
	Ewh Whyalla Sandstone	- M.g. red sandstone.
	E-p? Pandurra Fm.	- Grey and red; m.g. pebbly grit to sandstone with thinly bedded red shale interbeds. Heavy mineral banding and red shale clasts common.
	Ecr? Roopena Volcanics	- Red to grey; v.c.g. altered amy. or fragmental mafic volcanic, composed of ab and epi and quartz and chl. and hem. Some sections rich in red Kf. v.f.g. py and native Cu (?).

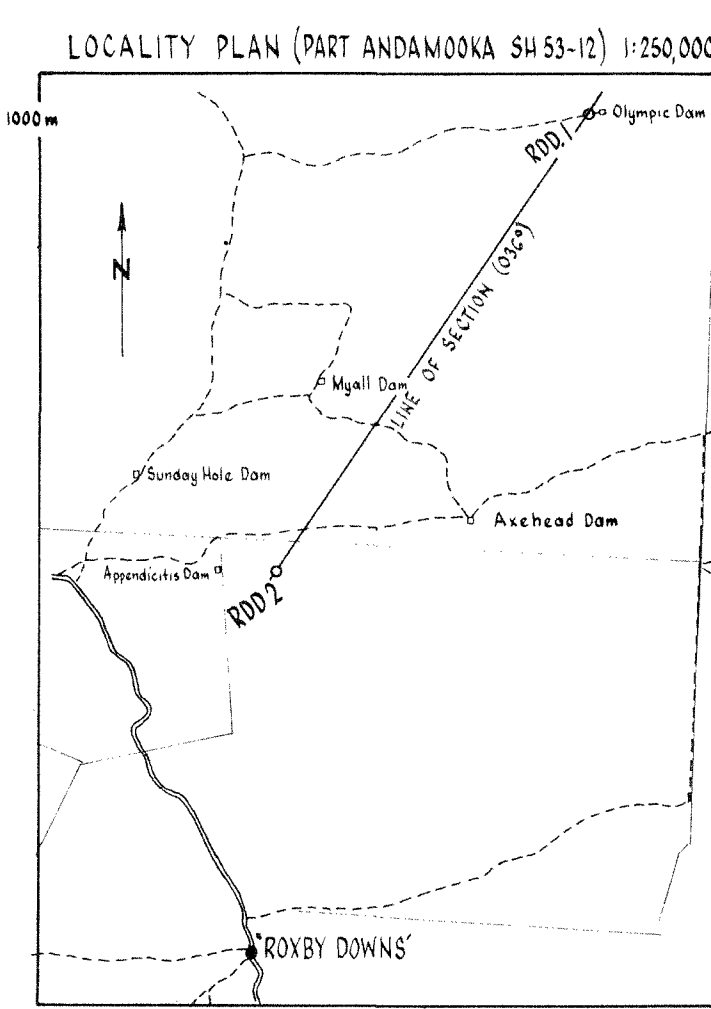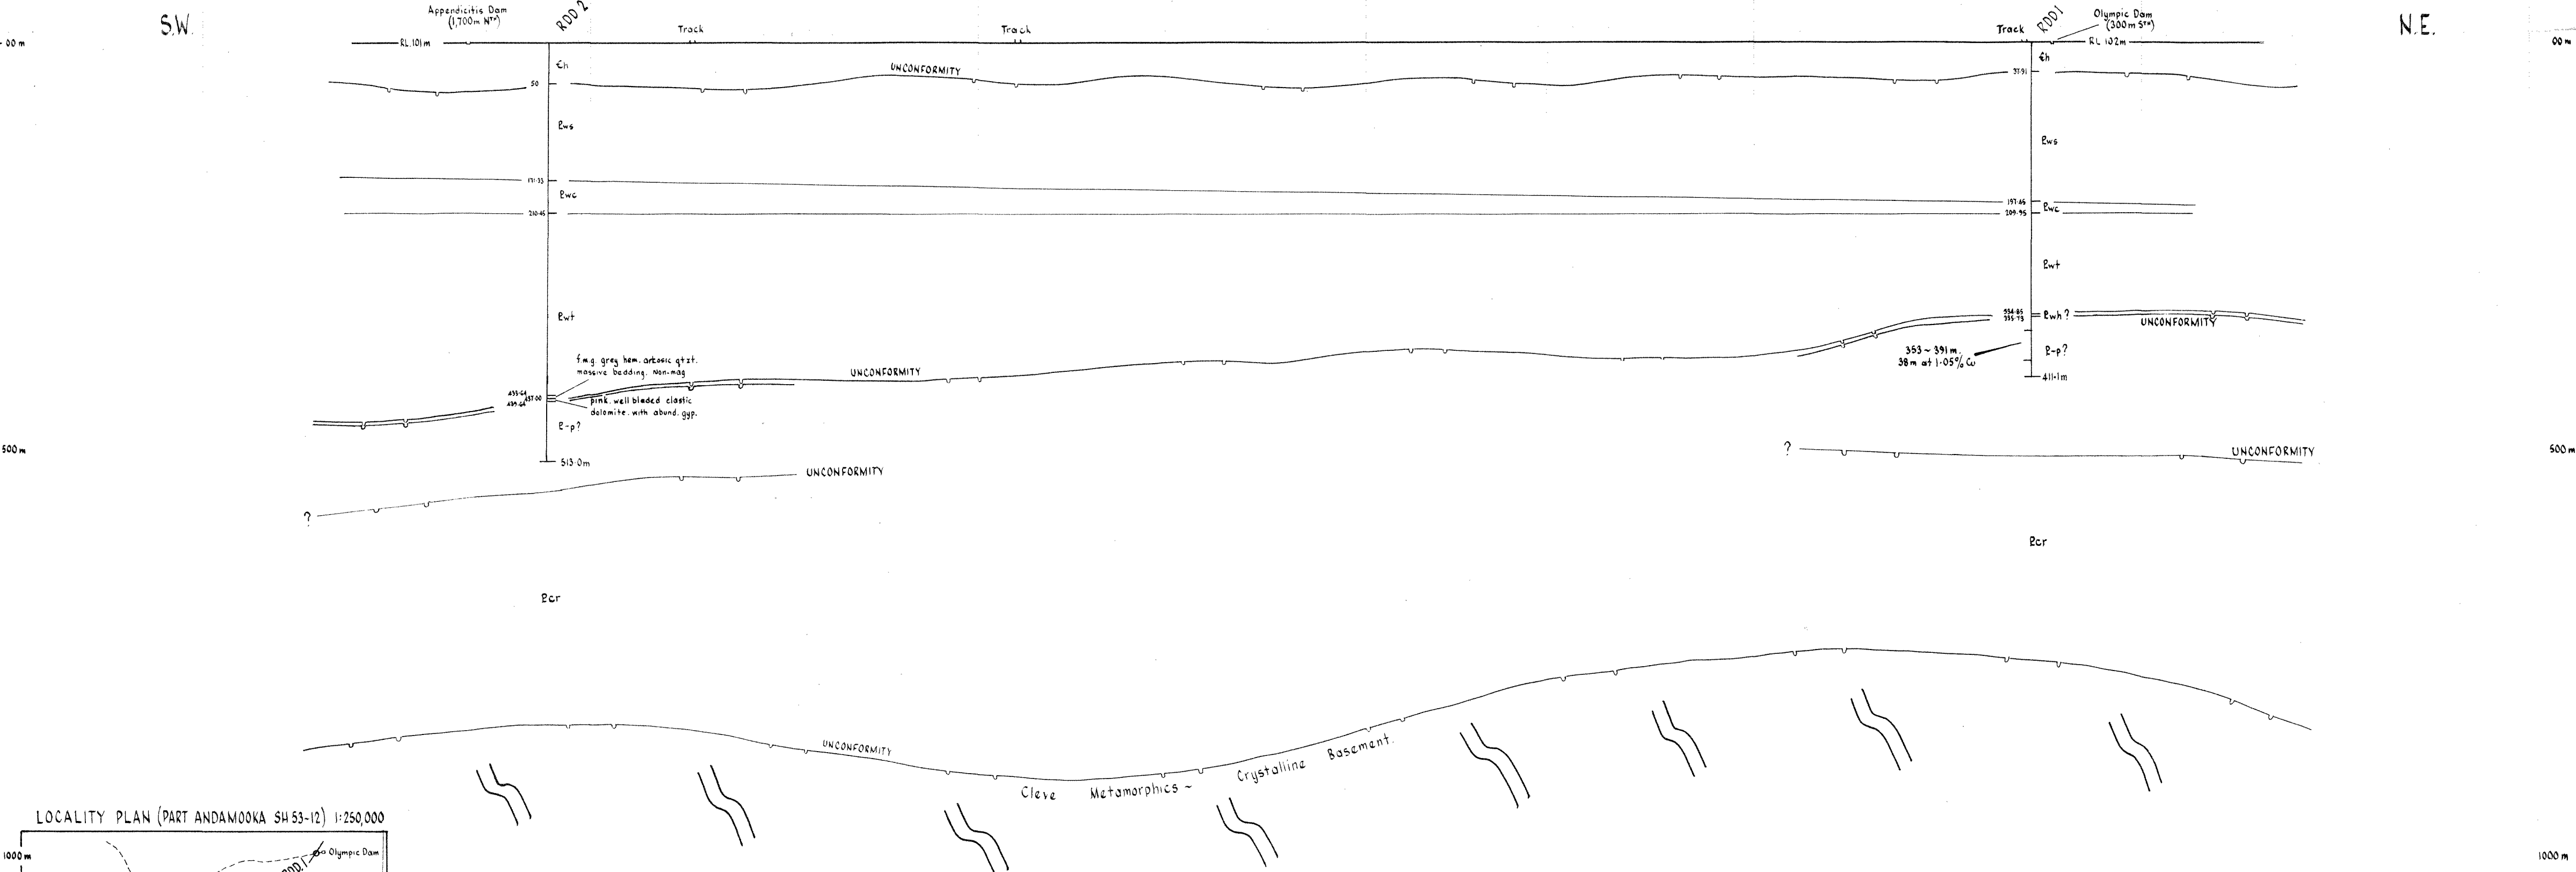

WESTERN MINING CORPORATION LIMITED		
ANDAMOOKA(SA) EL 190		
STRATIGRAPHIC DIAMOND DRILLING		
CROSS SECTION RDD 1 - RDD 2		
SCALE 1:5000 Vert. 1:50000 Hor	DATE. OCT. 75	PLAN No 2307-02

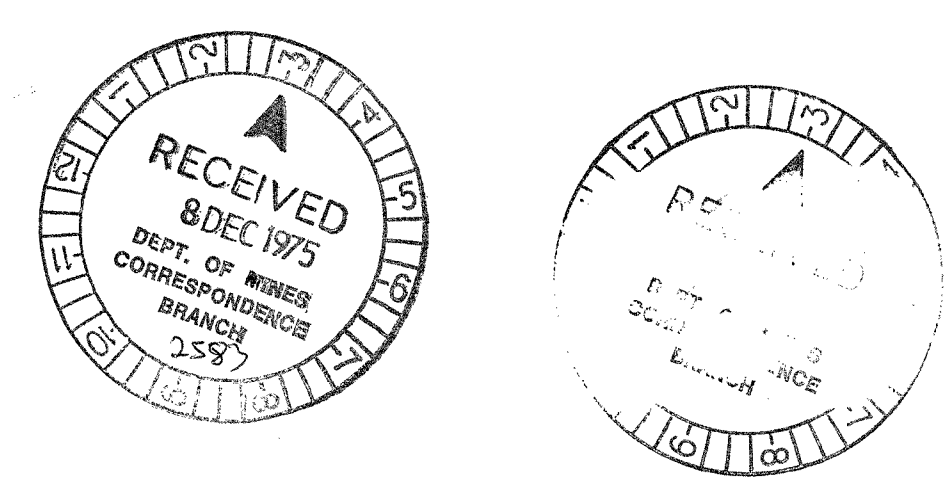

Reading Interval 90m
F.S. 1, 2, 10-19
(Uncorrected for geomagnetic gradient)

NANOTESLAS

63000

62000

61000

60000

59000

58000

57000

56000


70,000N 71 72 73 74 75 76 77 78 79 80,000N 81 82 83 84 85 86 87 88 89 90,000N 91 92 93 94 95 96 97 98 99 100,000N 101 102 103 104 105

TOTAL MAGNETIC INTENSITY PROFILE

BOUGUER ANOMALY PROFILE

SCALE 1:50,000

1000 500 0 1000 2000 3000 4000 5000
METRES

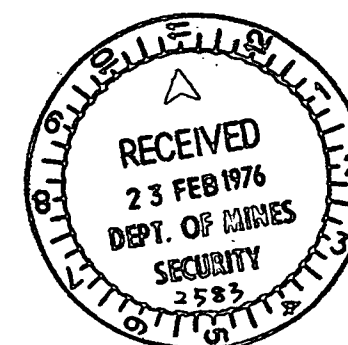

Reading Interval 90m
Density 2.20g/cm³
E.C.F. 2081 mg/m
Datum, Olympic Dam, 30m
F.S. 1, 2, 5, 9-15, 21-25

MILLIGALS

-10

-12

-14

-16

-18

-20

-22

-24

-26

-28

-30

WESTERN MINING CORPORATION LIMITED

ANDAMOOKA (S.A.) E.L. 190

BOUGUER ANOMALY PROFILE

TOTAL MAGNETIC INTENSITY PROFILE

LINE 100,000E

DATE: December 1975

SCALE: 1:50,000


PLAN No 2307-09

Reading Interval 90m
F.S. 22-25m
(Uncorrected for geomagnetic gradient)

NANOTESLAS


Reading Interval 90m
Density 2.20 g/c³
E.C.F. 2081 mg/m
Datum Olympic Dam, 30 m
F.S. 16-19

MILLIGALS

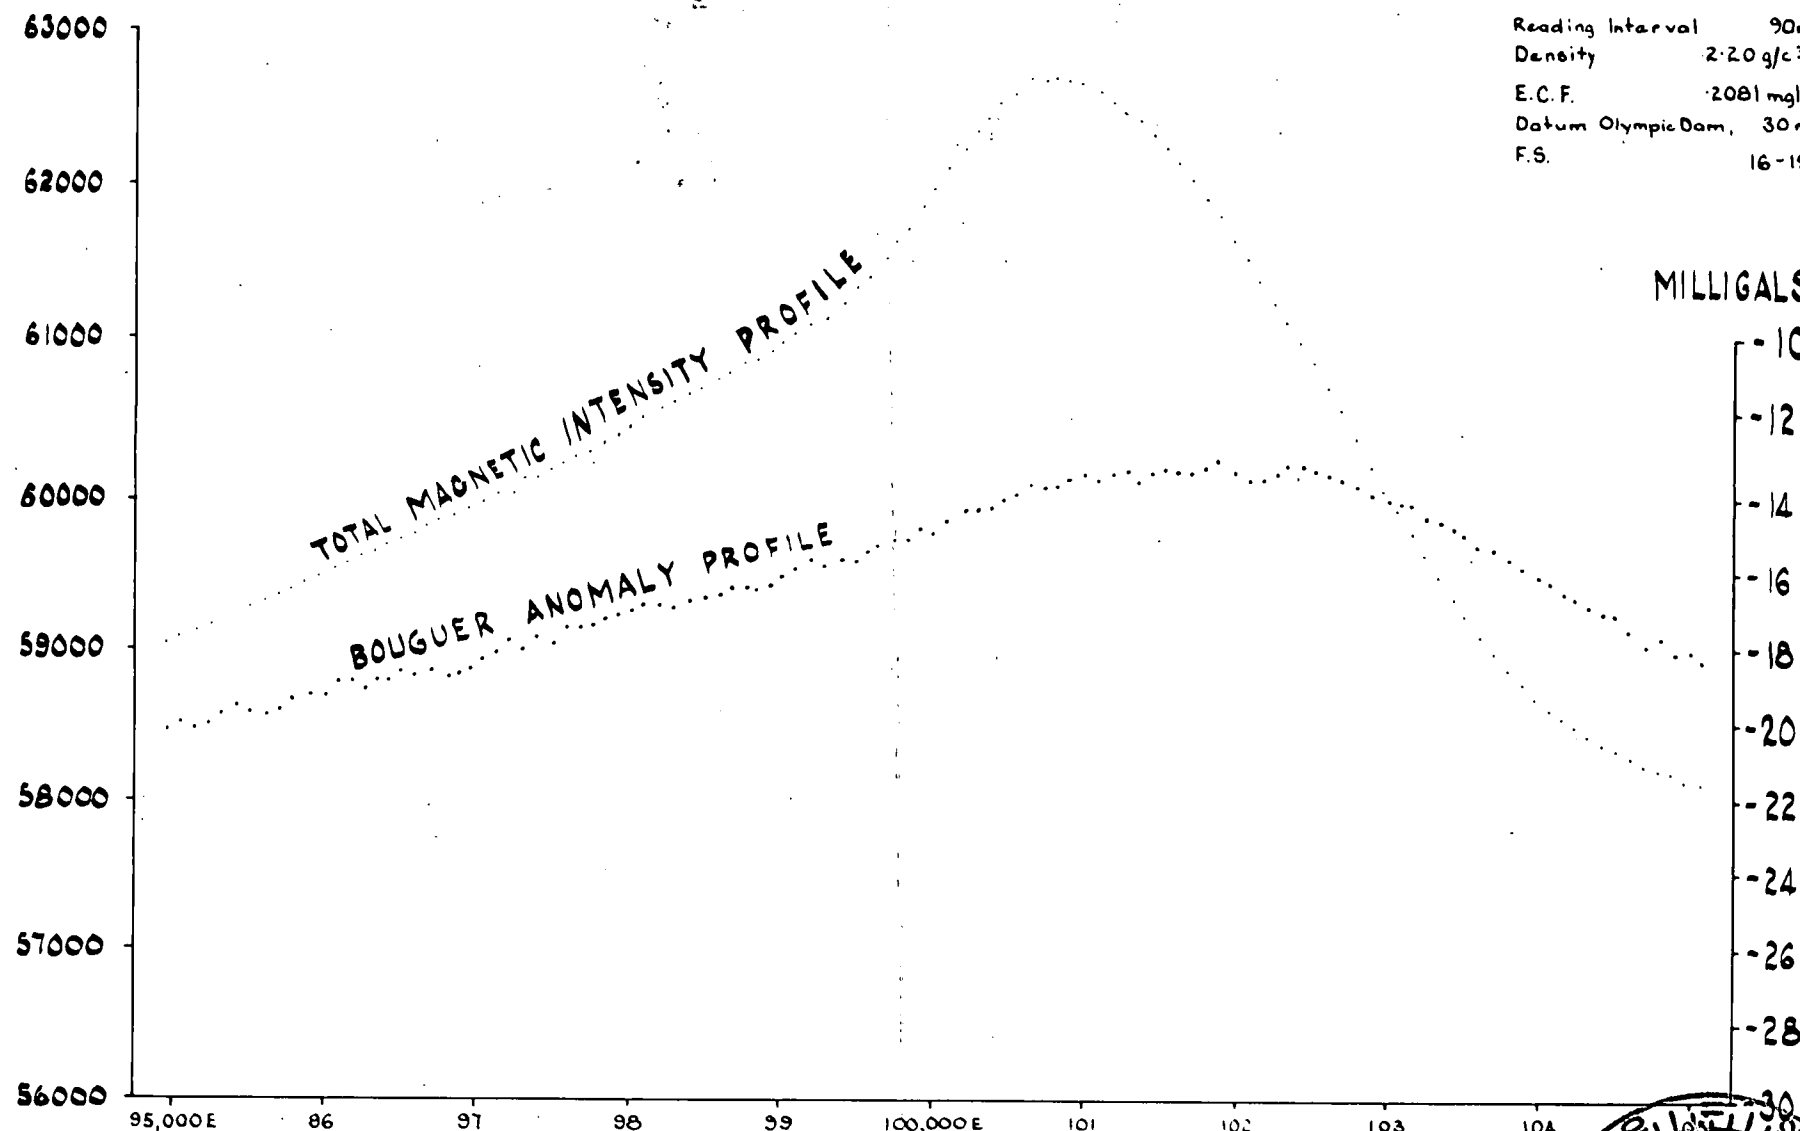

SCALE 1:50,000

1000 500 0 1000 2000 3000 4000 5000
METRES

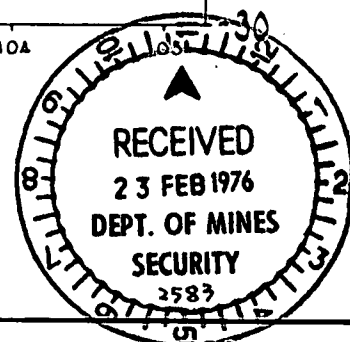

WESTERN MINING CORPORATION LIMITED

ANDAMOOKA (S.A) E.L. 190

BOUGUER ANOMALY PROFILE

TOTAL MAGNETIC INTENSITY PROFILE

LINE 82,000N

DATE: December 1975

SCALE 1:50,000

PLAN NO: 2307-10

Reading Interval 90m
F.S. 3-9, 21, 22
(Uncorrected for geomagnetic gradient)

NANOTESLAS

59000

58000

57000

56000

80

81,000 E

82

83

84

85

86

87

88

89

90,000 E

91

92

93

94

95

96

97

98

99

100,000 E

101

102

103

104

105

TOTAL MAGNETIC INTENSITY PROFILE

BOUGUER ANOMALY PROFILE

SCALE 1:50,000

1000 500 0 1000 2000 3000 4000 5000
METRES

Density 2.20 g/cc
Reading Interval 90 m
E.C.F. -2081 mgl/m
Datum, Olympic Dam, 30 m
F.S. 3, 4, 6-8, 21-34

MILLIGALS

-14

-16

-18

-20


-22

-24

-26

-28

-30

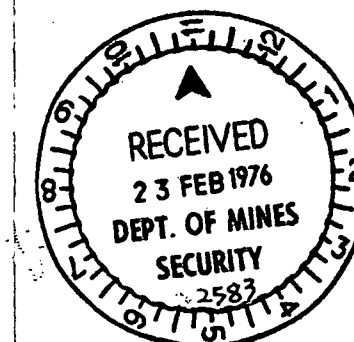

WESTERN MINING CORPORATION LIMITED

ANDAMOOKA (S.A.) E.L. 190

BOUGUER ANOMALY PROFILE

TOTAL MAGNETIC INTENSITY PROFILE

LINE 100,000N

DATE: December 1975

SCALE: 1:50,000.

PLAN No: 2307-11